




BANKS-SP / BANK-A

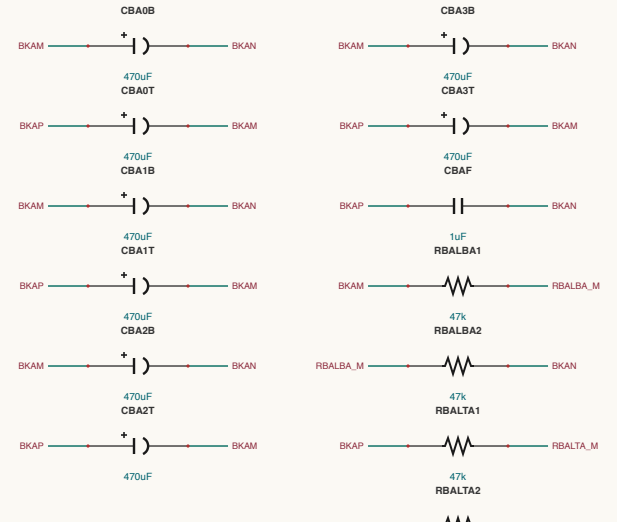


BANKS-SP / BANK-B

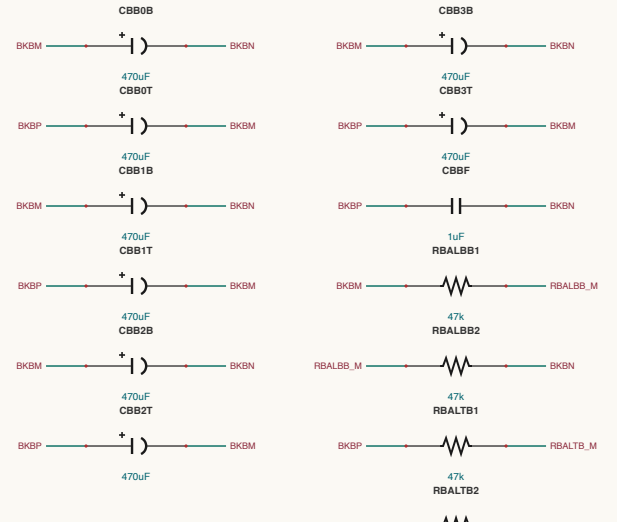


BANKS-SP / SP-MATRIX

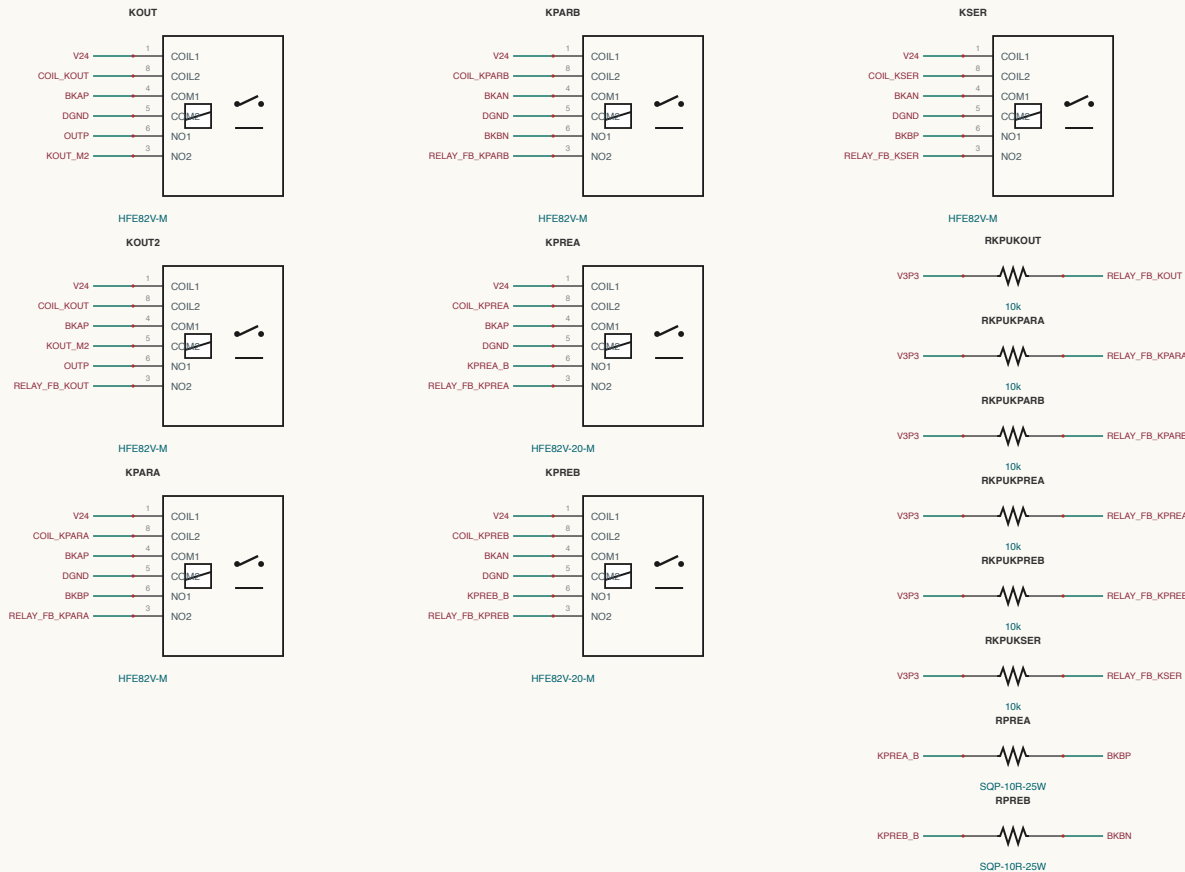


LLC-LESS / LEO-1

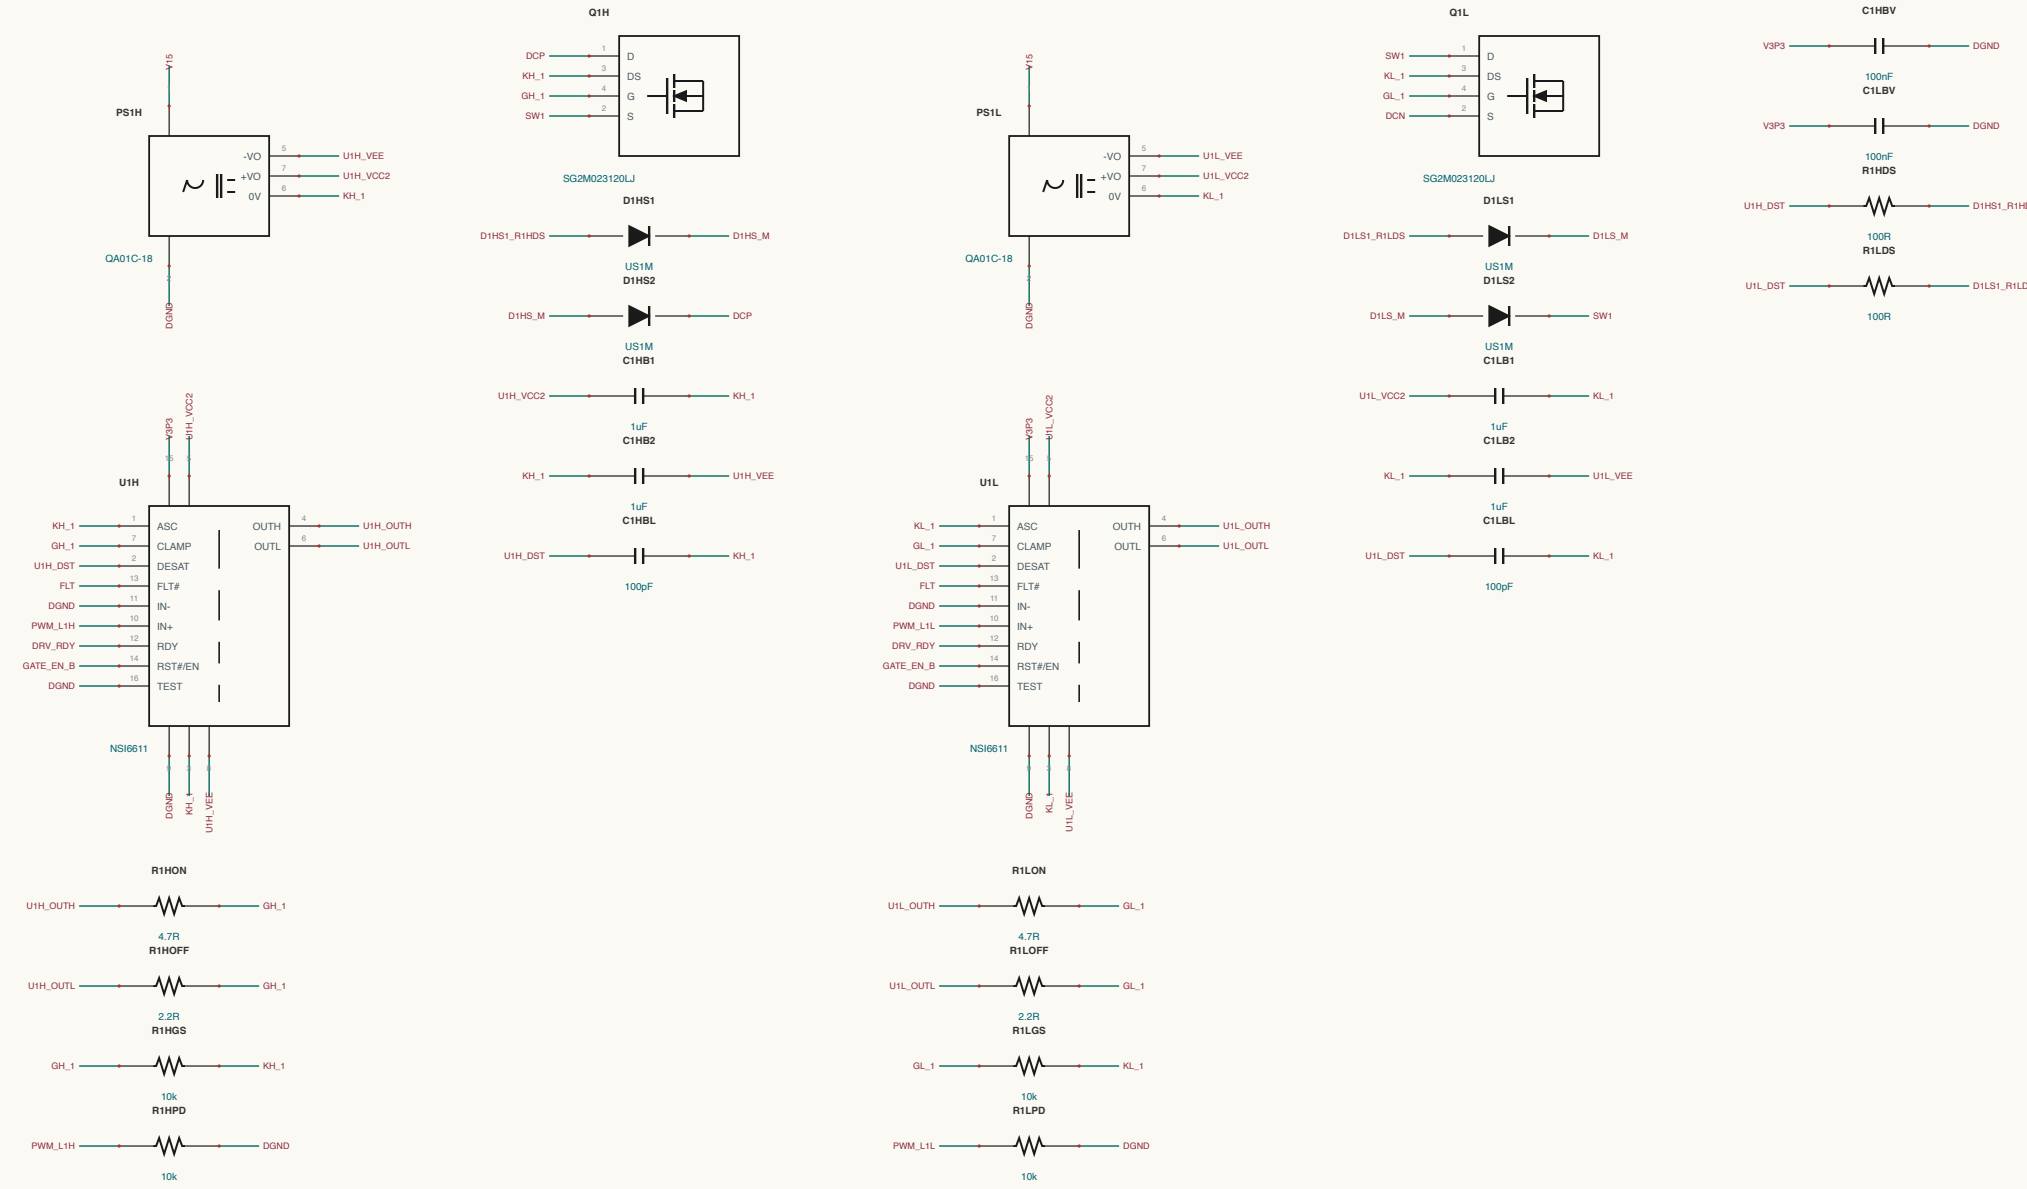


LLC-TANKS / TANK-1

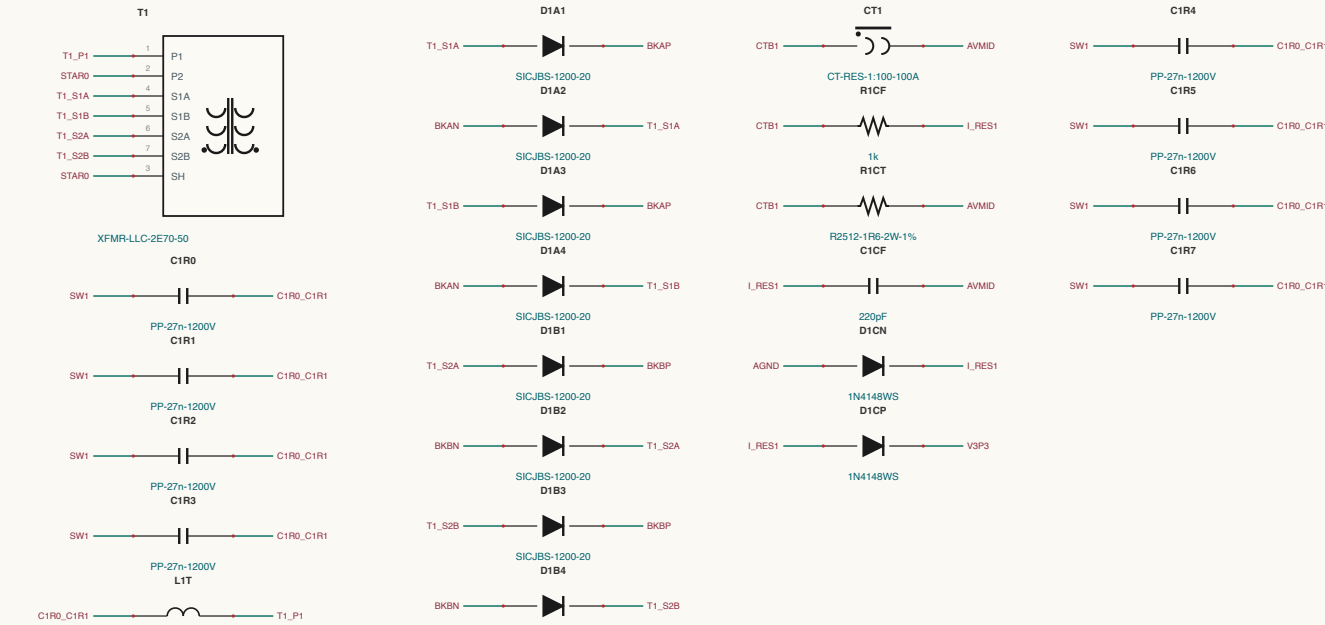


BANKS-SP / BLEEDERS

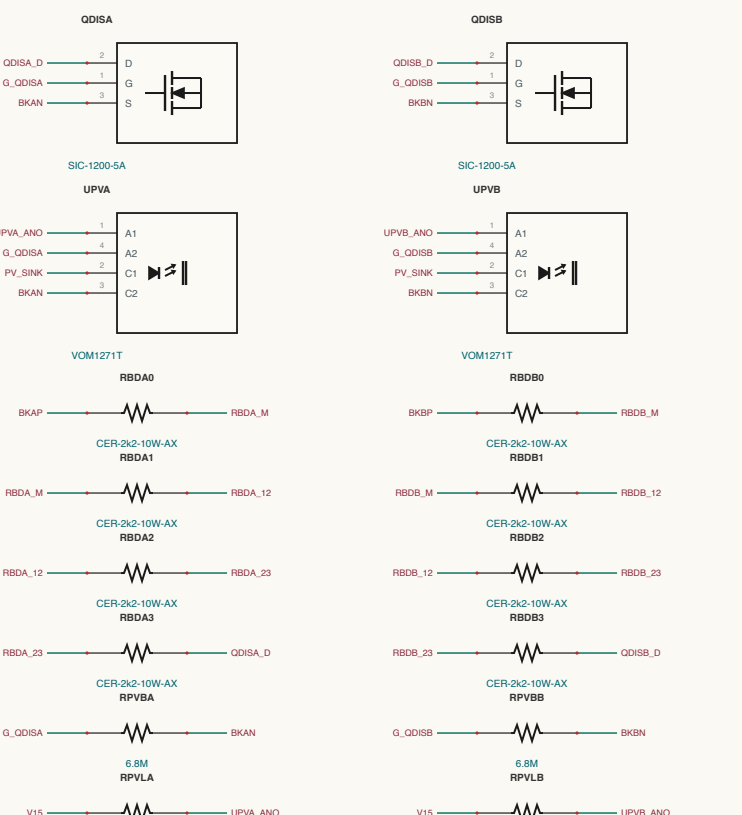


COMMS-HUB / HUB

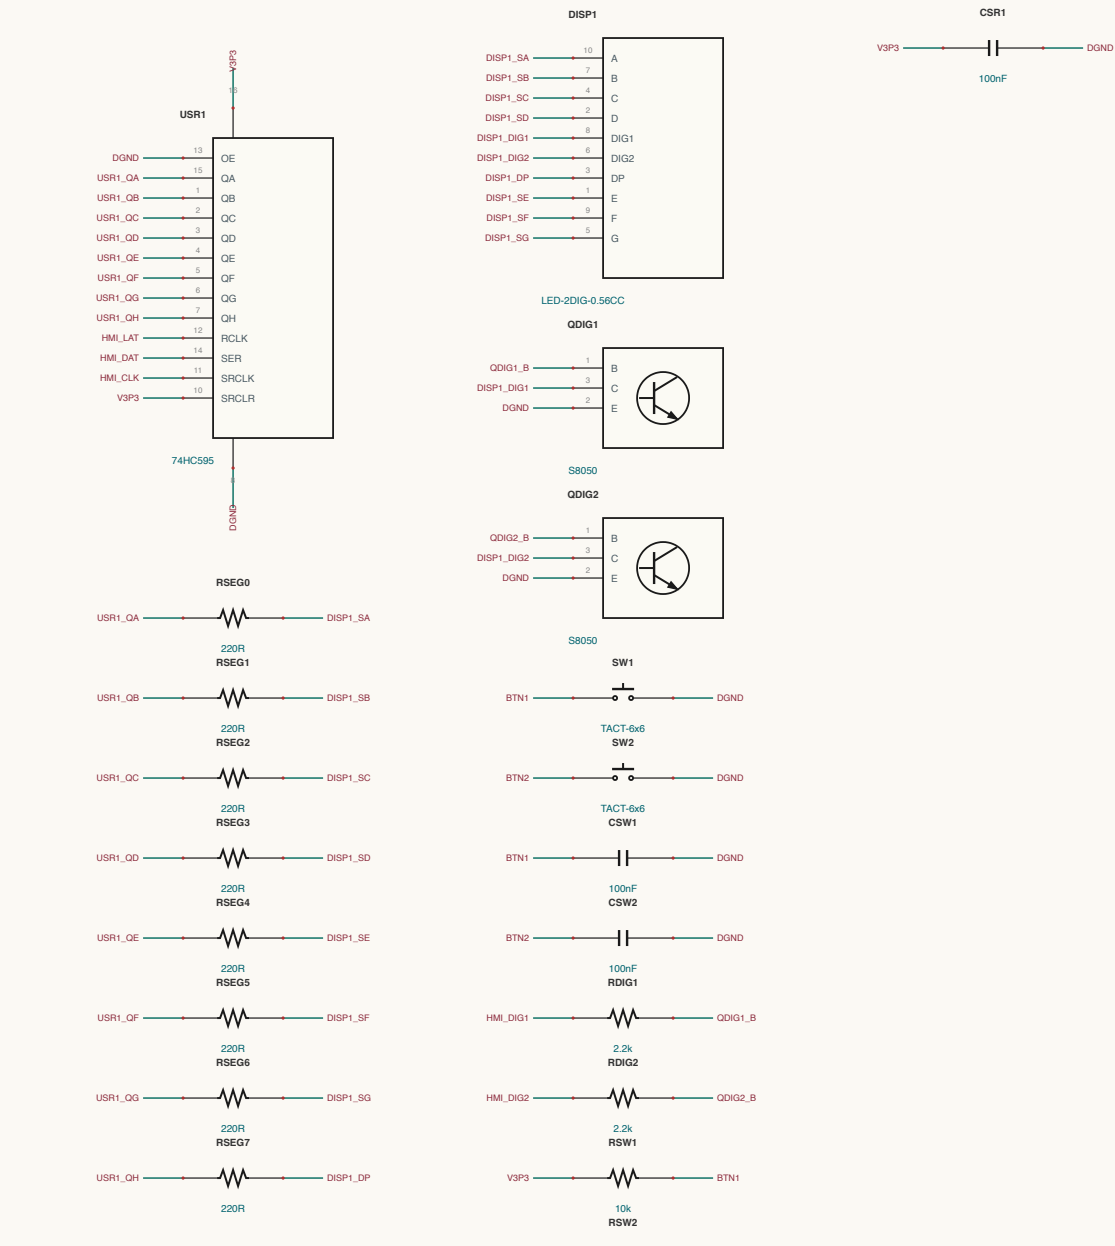


LLC-LESS / LEO-2

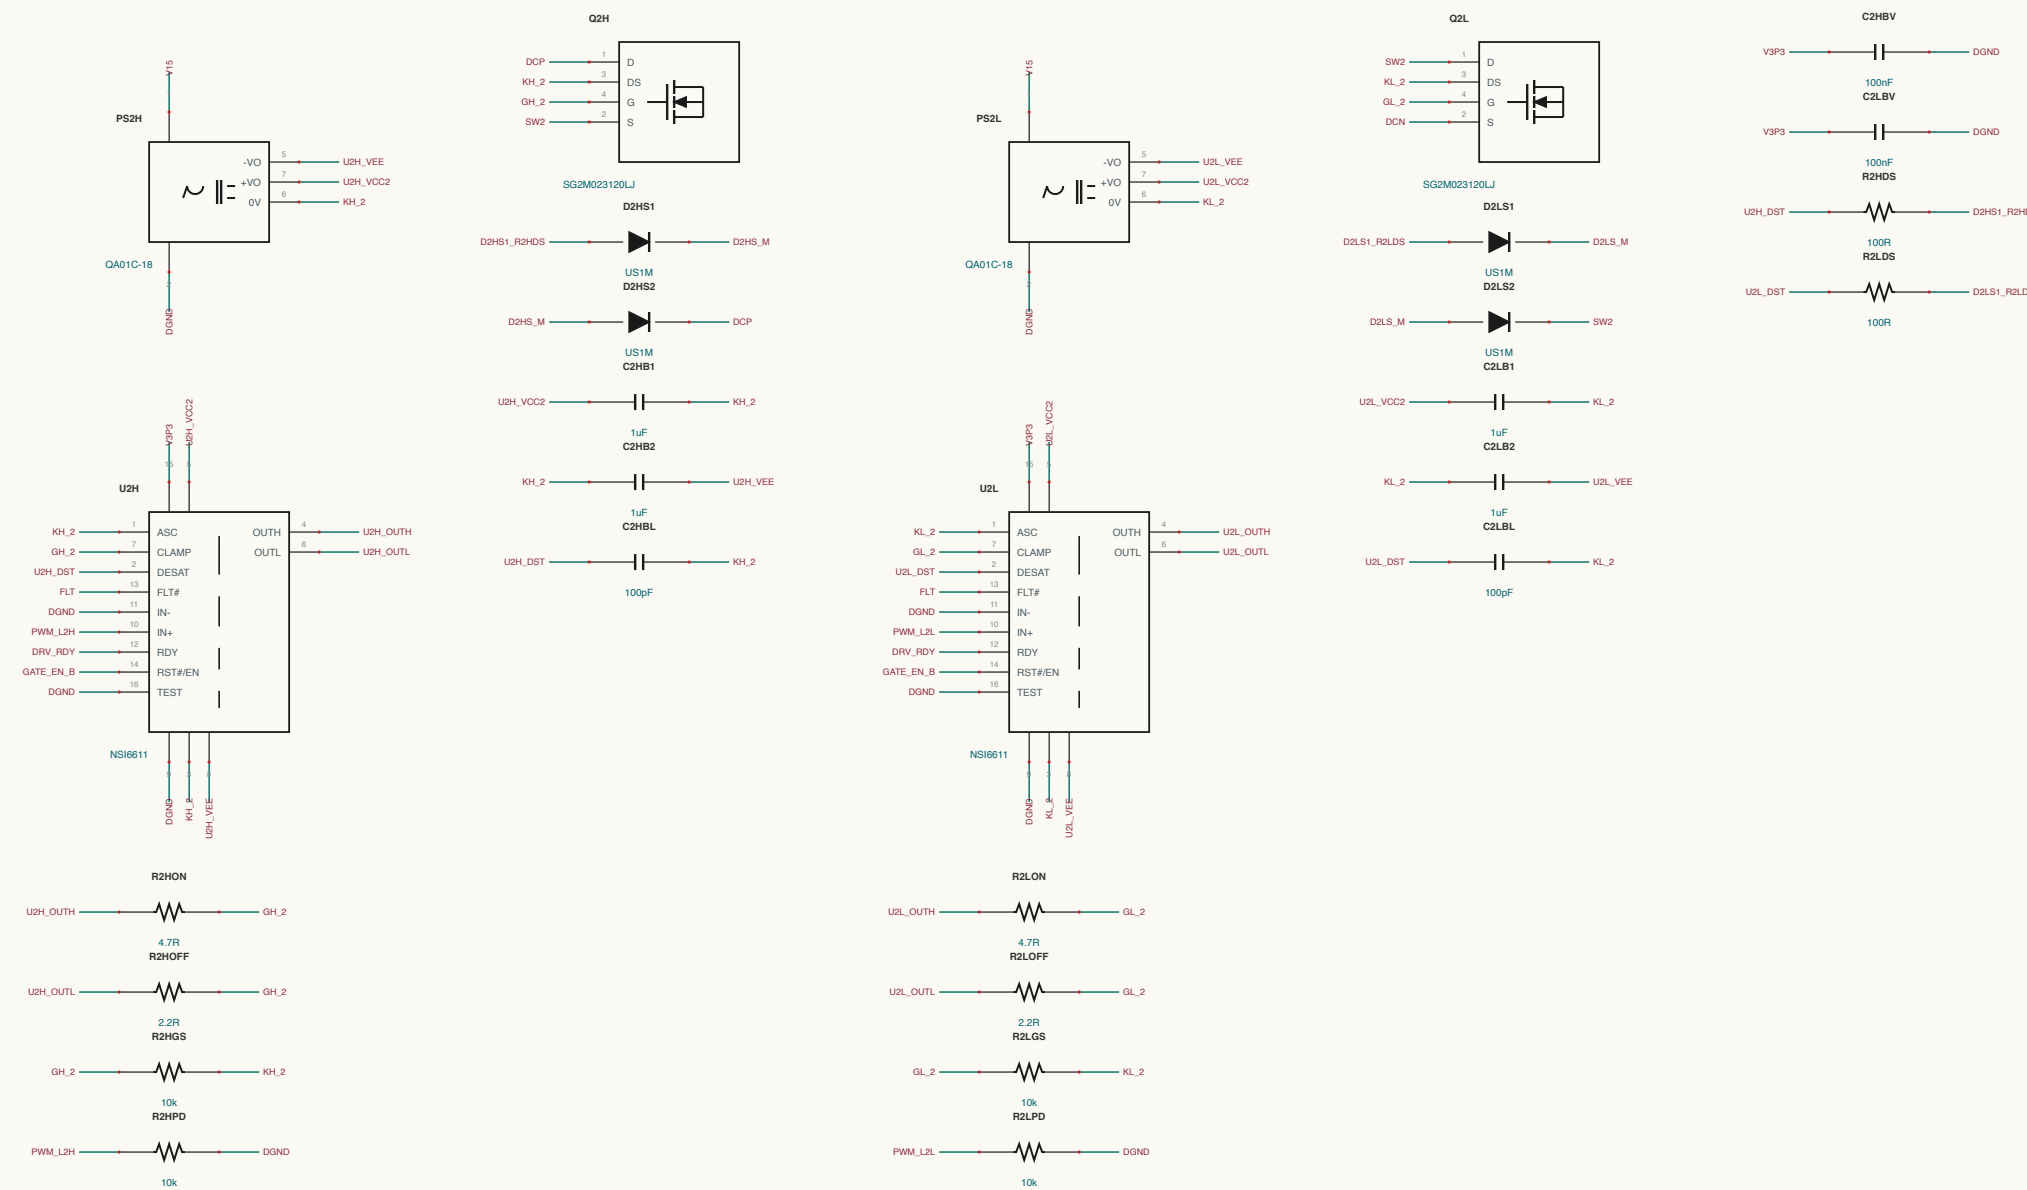


LLC-TANKS / TANK-2

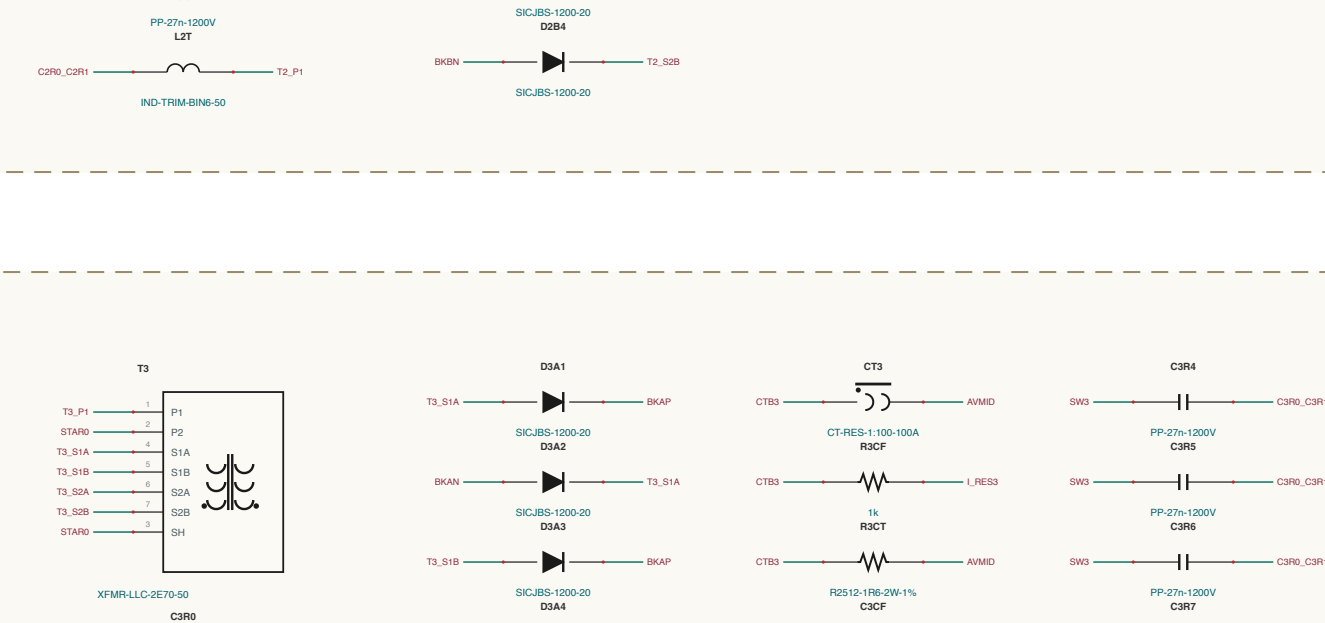


COMMS-HUB / CAN

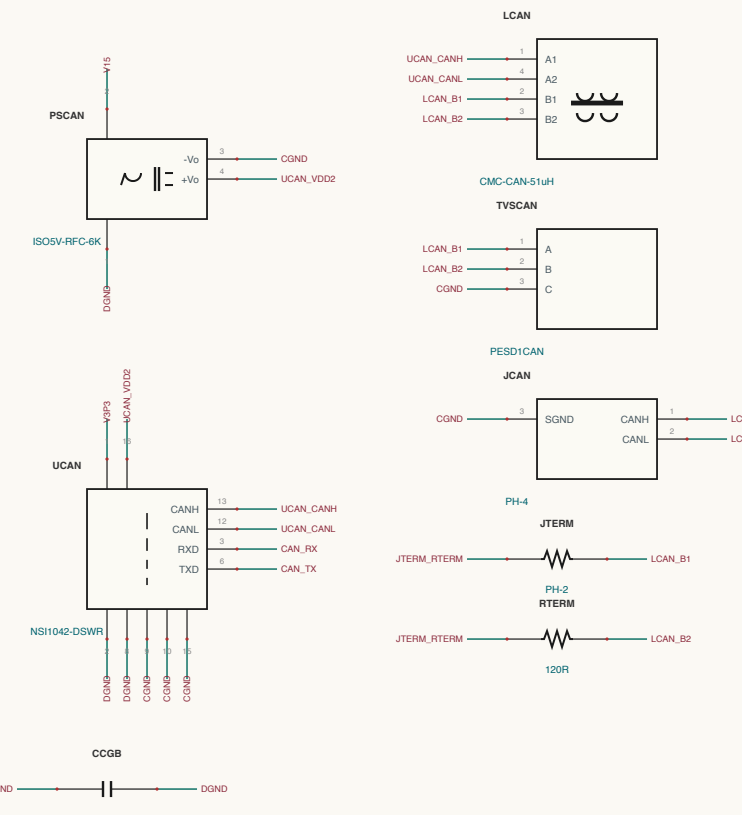


LLC-TANKS / TANK-3

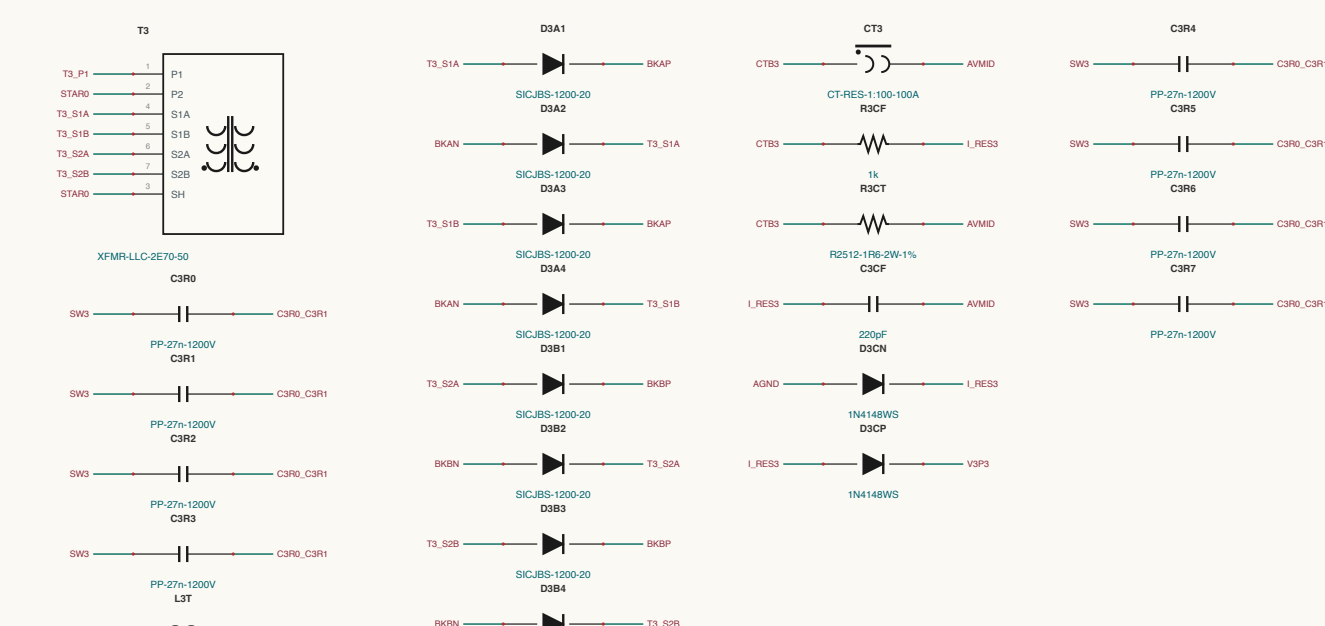


CONTROL / CARD-F

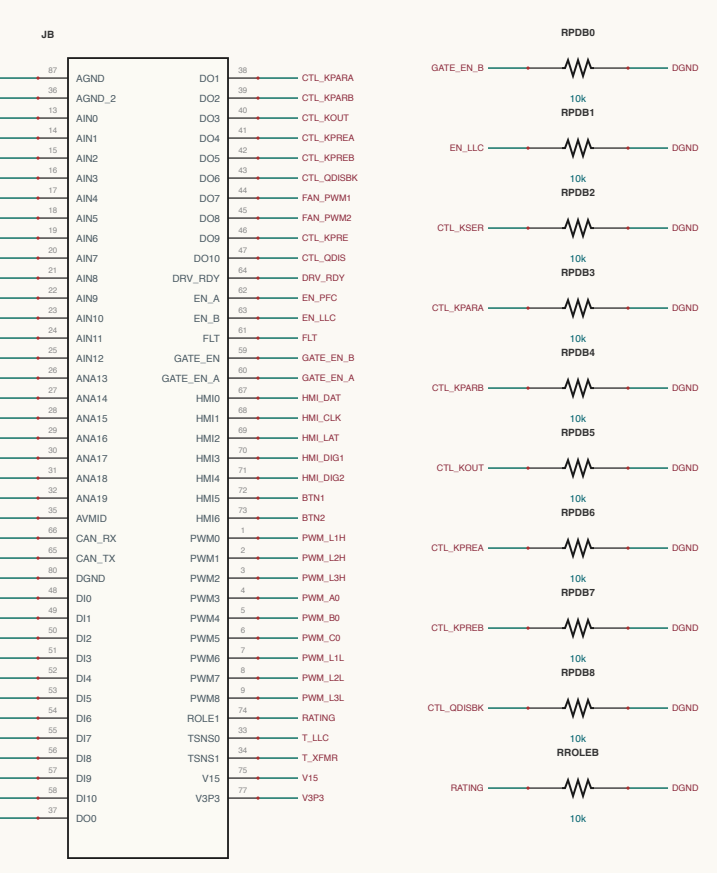


LLC-LESS / BUS-R

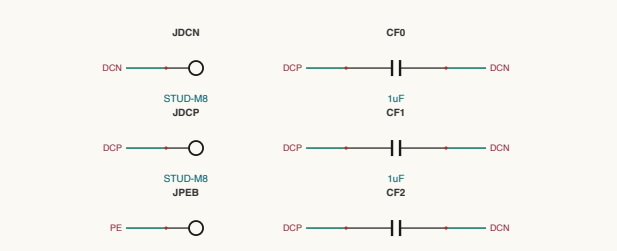


CONTROL / COL-DRIVER

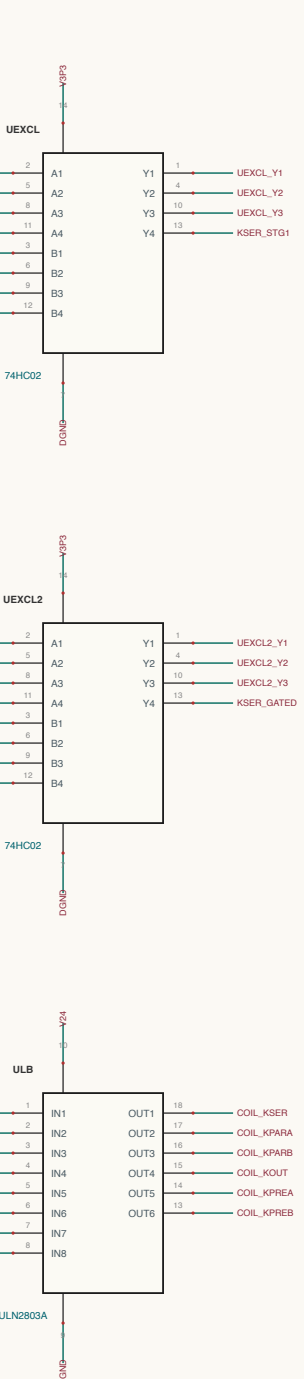


CONTROL / INTERCONNECT

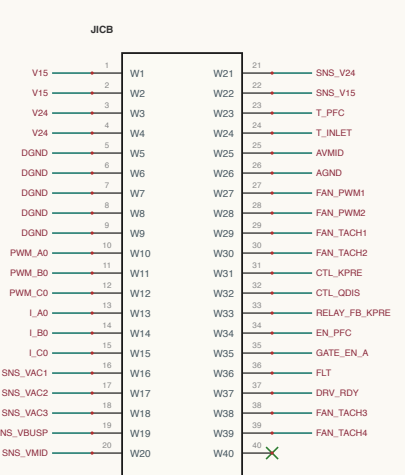


LLC-LESS / LEO-3

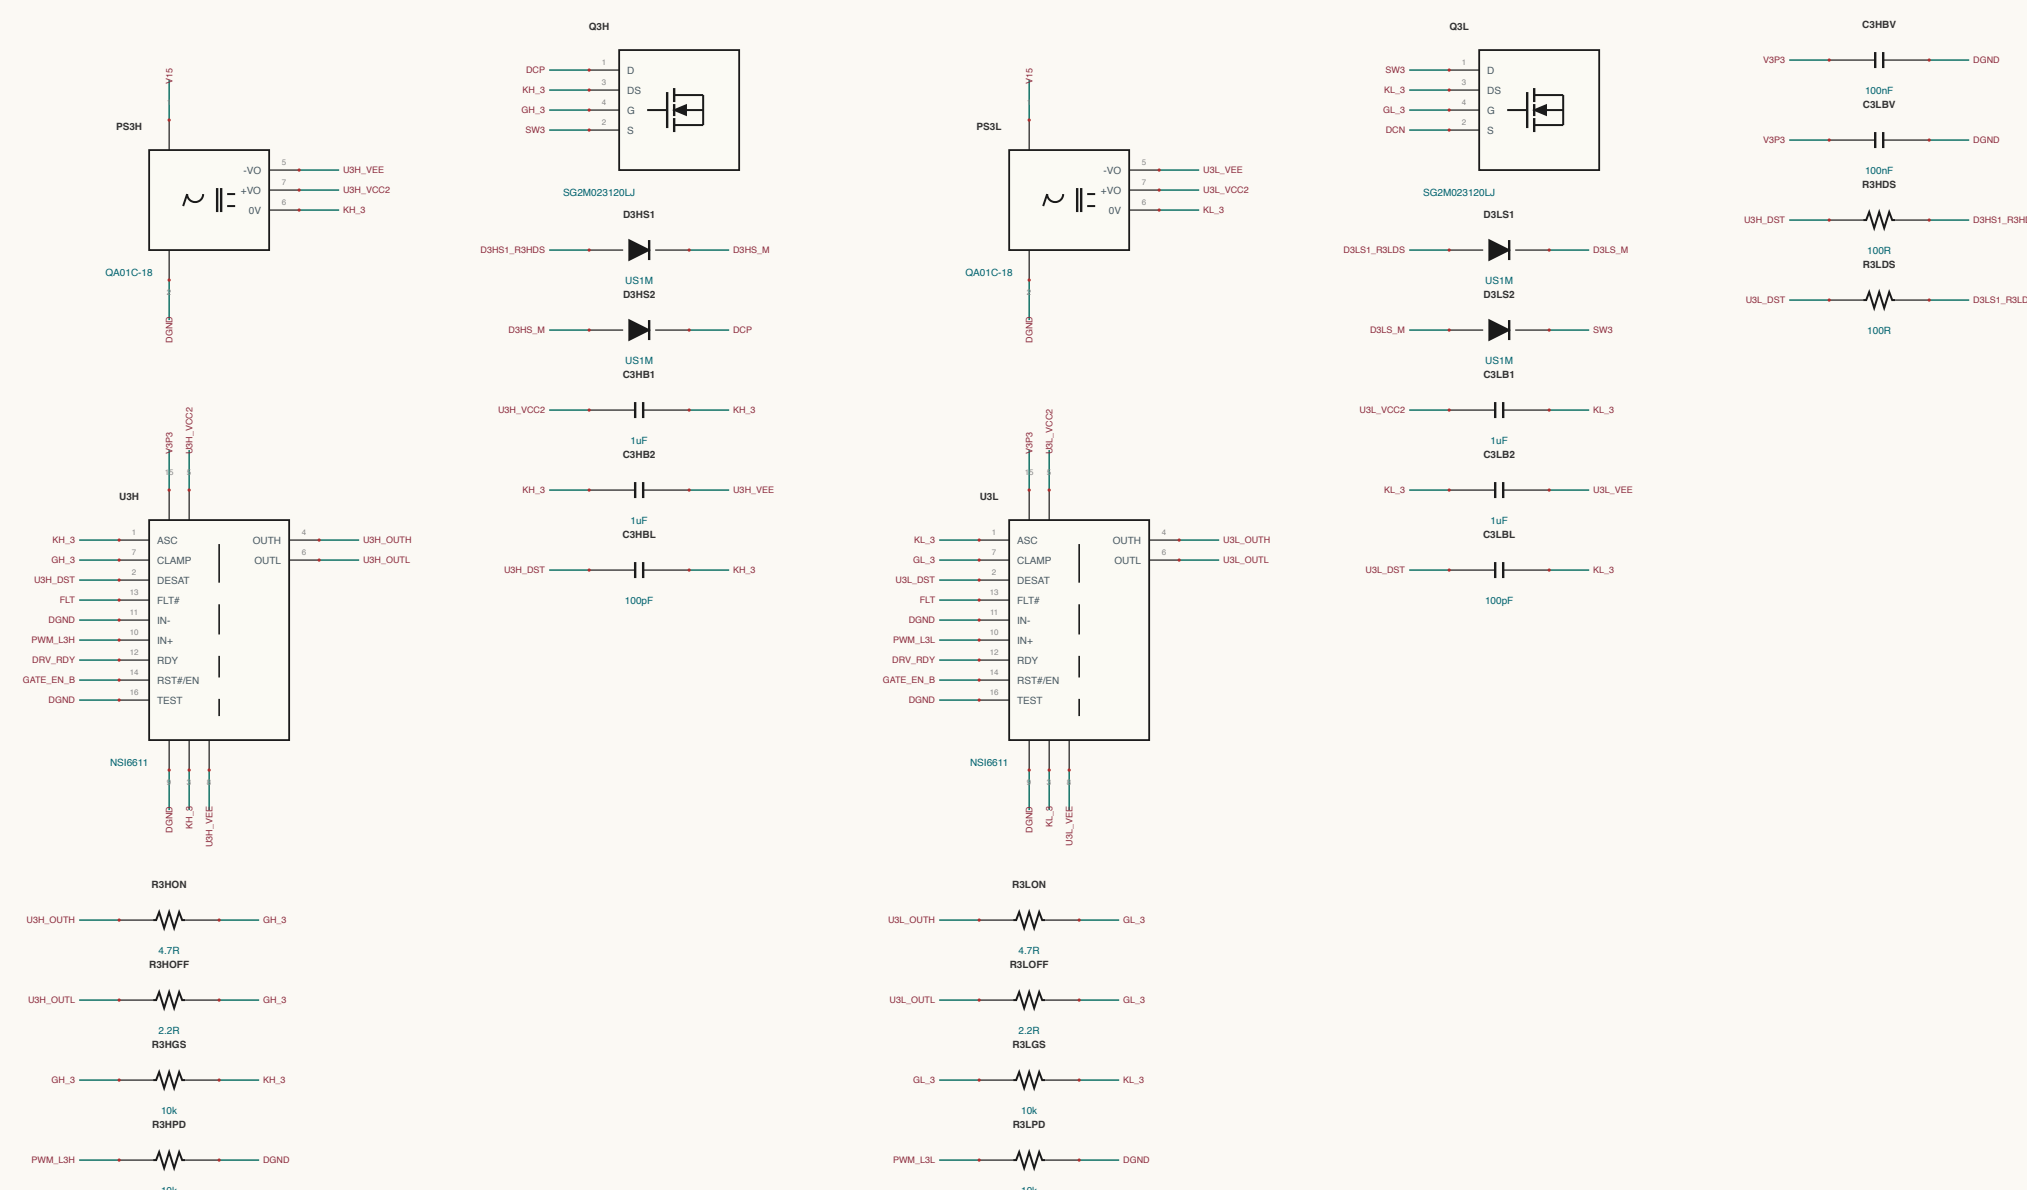


OUTPUT-SENSING / OUTPUT

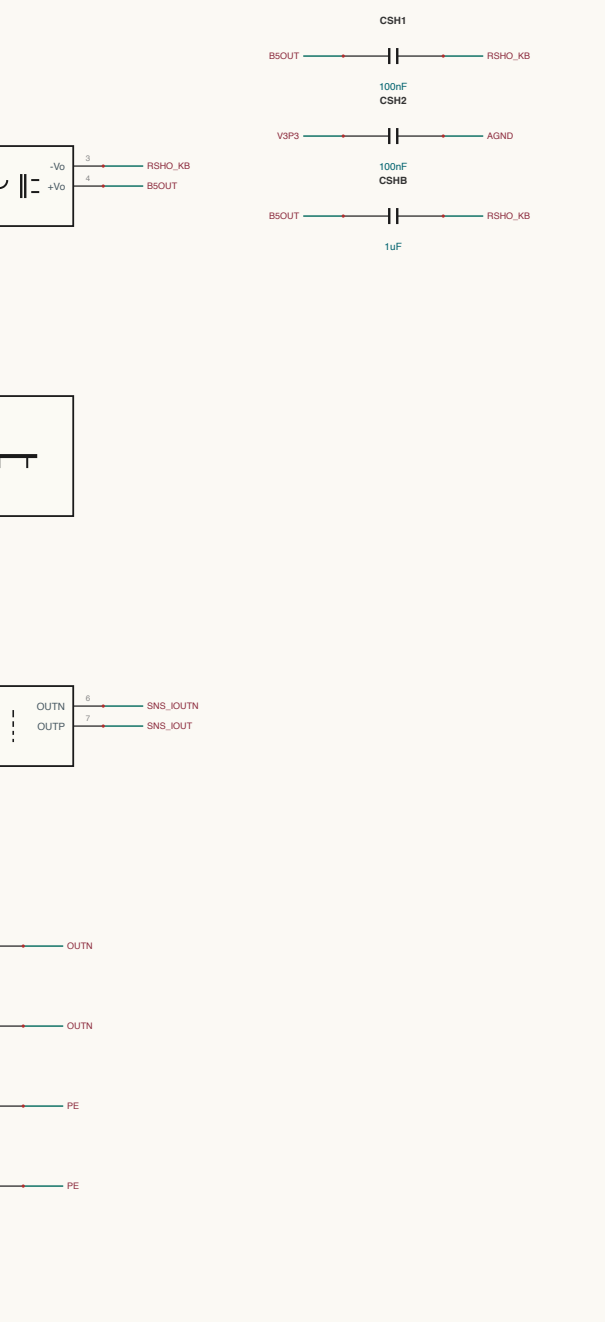


OUTPUT-SENSING / SENSE-VOLTA

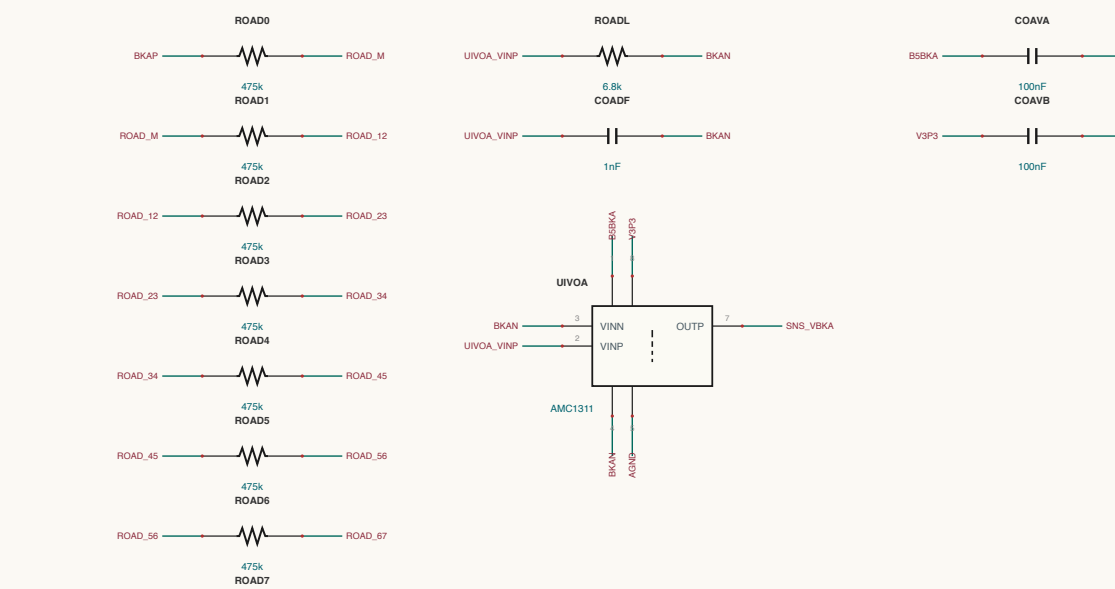

OUTPUT-SENSING / SENSE-VOLTA

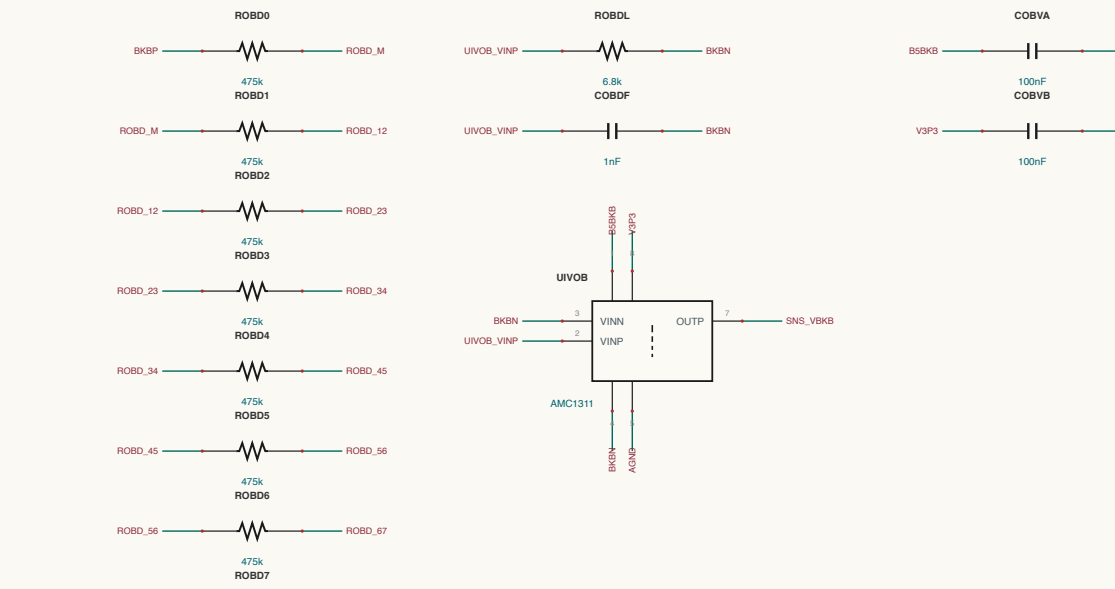


OUTPUT-SENSING / ISO-MAX

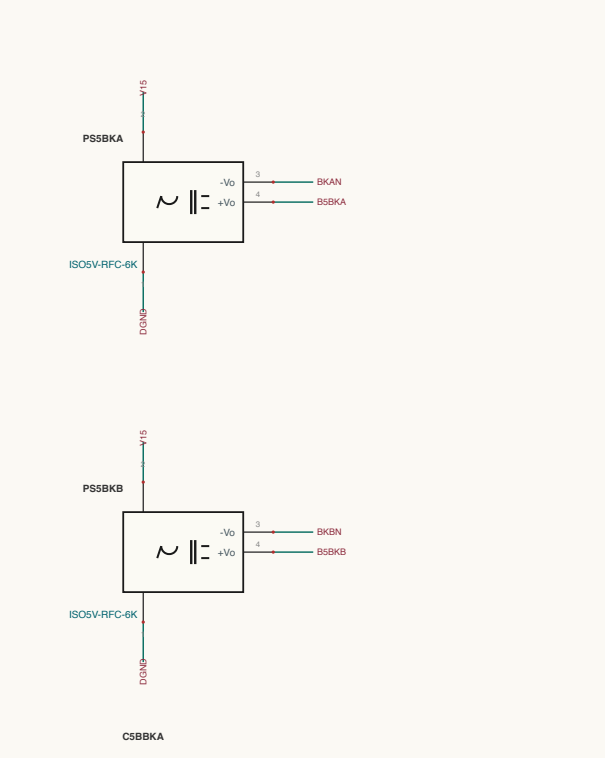


NET NAMING




MAGNETICS CONSTRUCTION

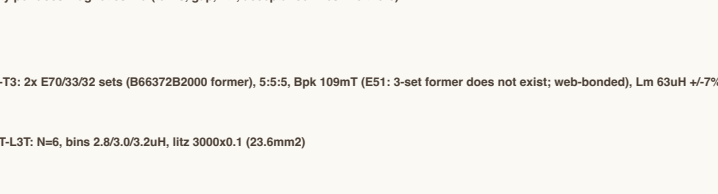

OUTPUT-SENSING / SENSE-VOUT

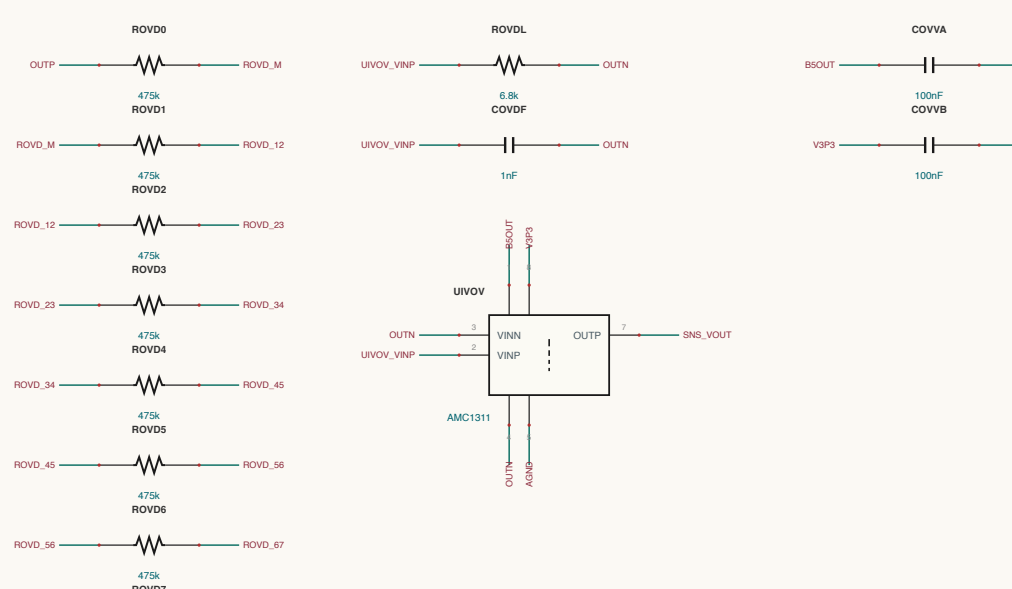

OUTPUT-SENSING / ATC

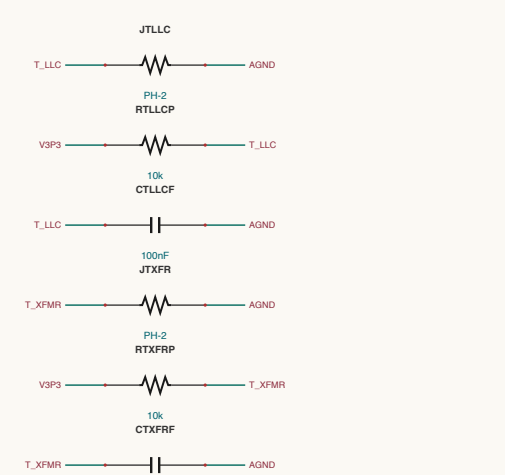

SHEET INDEX

